


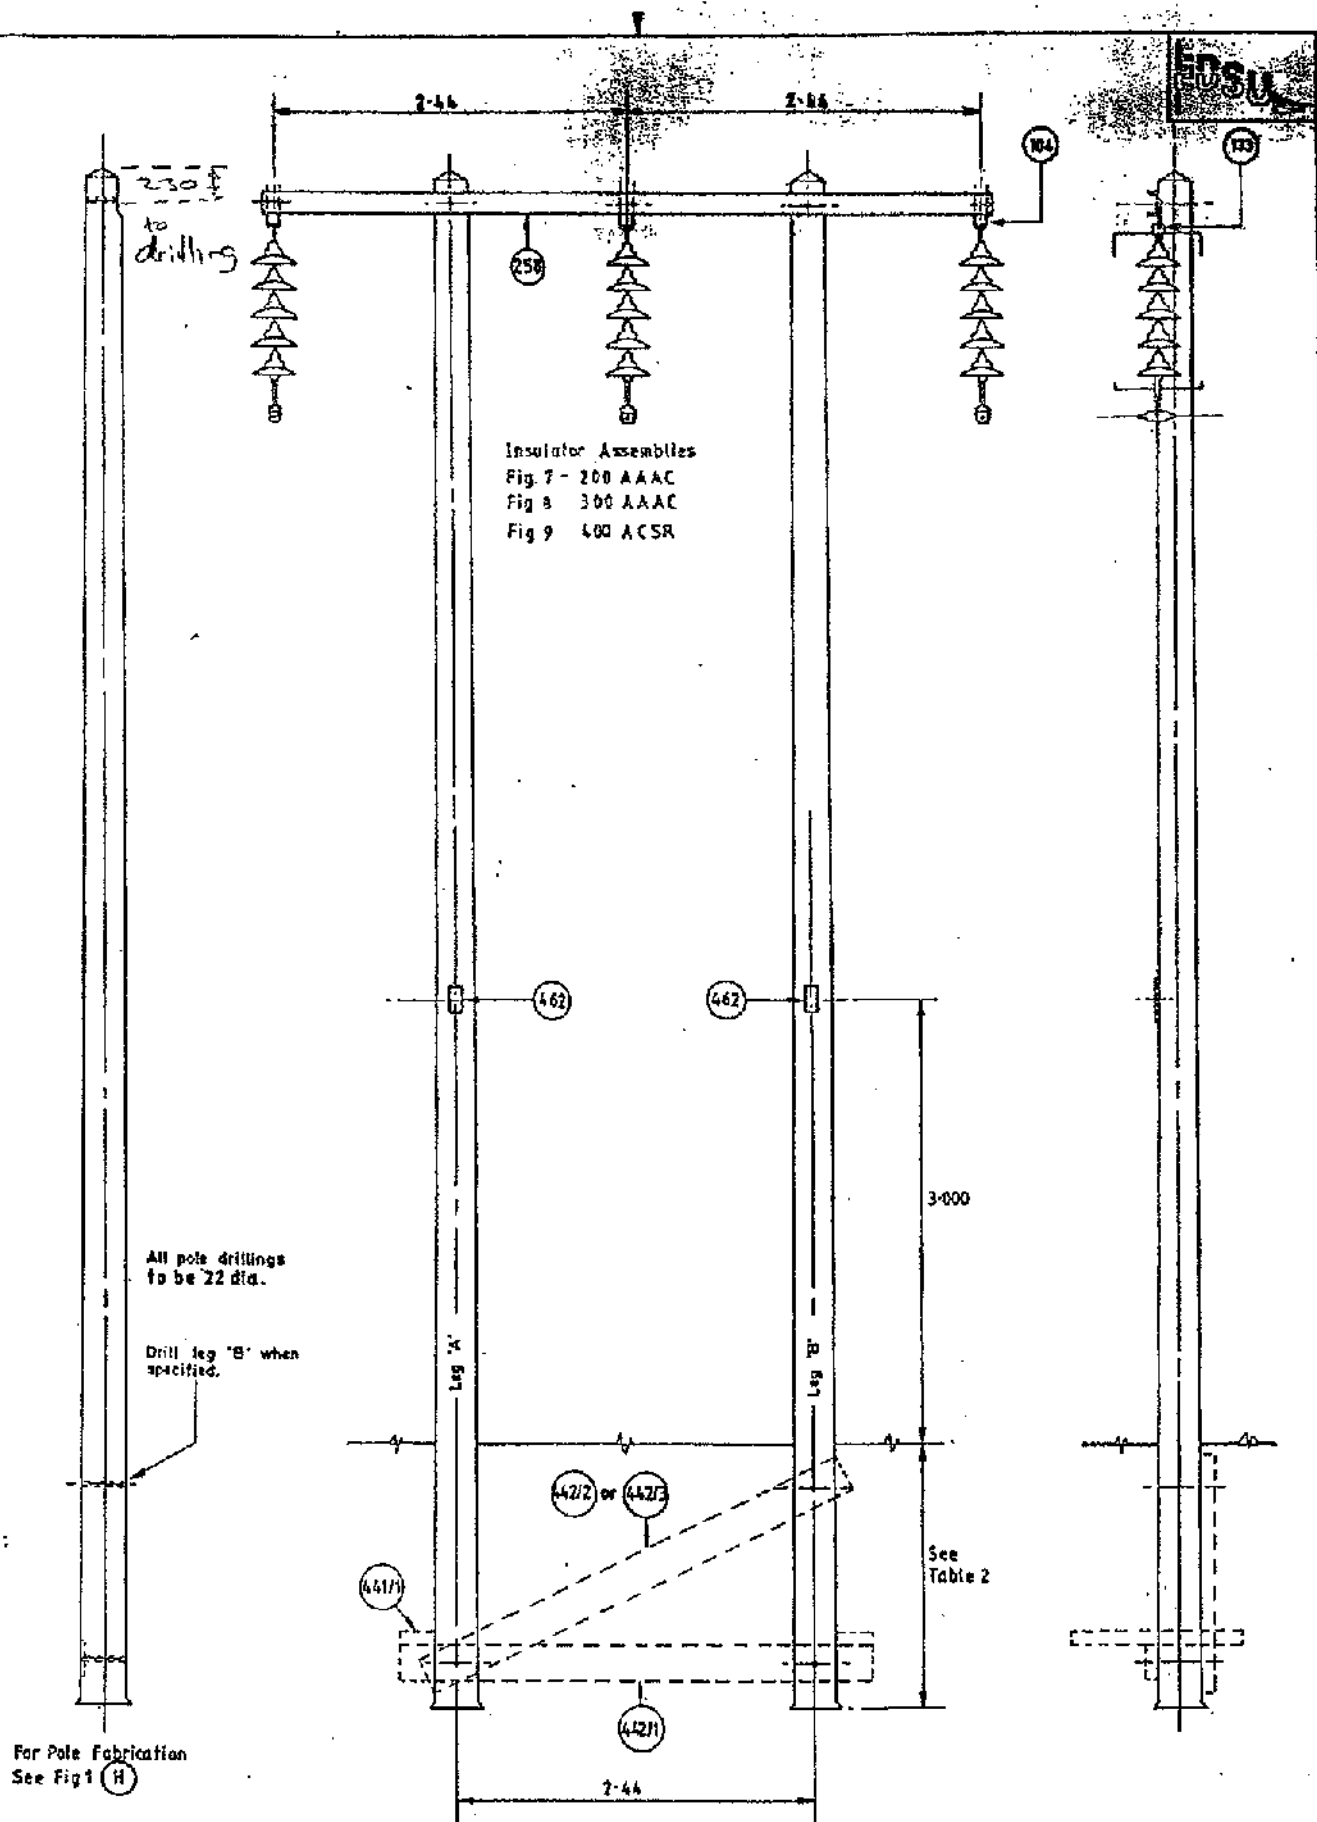

66kV CONSTRUCTION
 H SUSPENSION ST. LINE & THROUGH
 ANGLES UP TO 3°

SCALE	27.5:1
DATE	W. B.
EXAMIN	P. G.
TRACED	
CHECKED	
APPROVED	

MEB
 Midlands Electricity plc
 FIG. 2.