


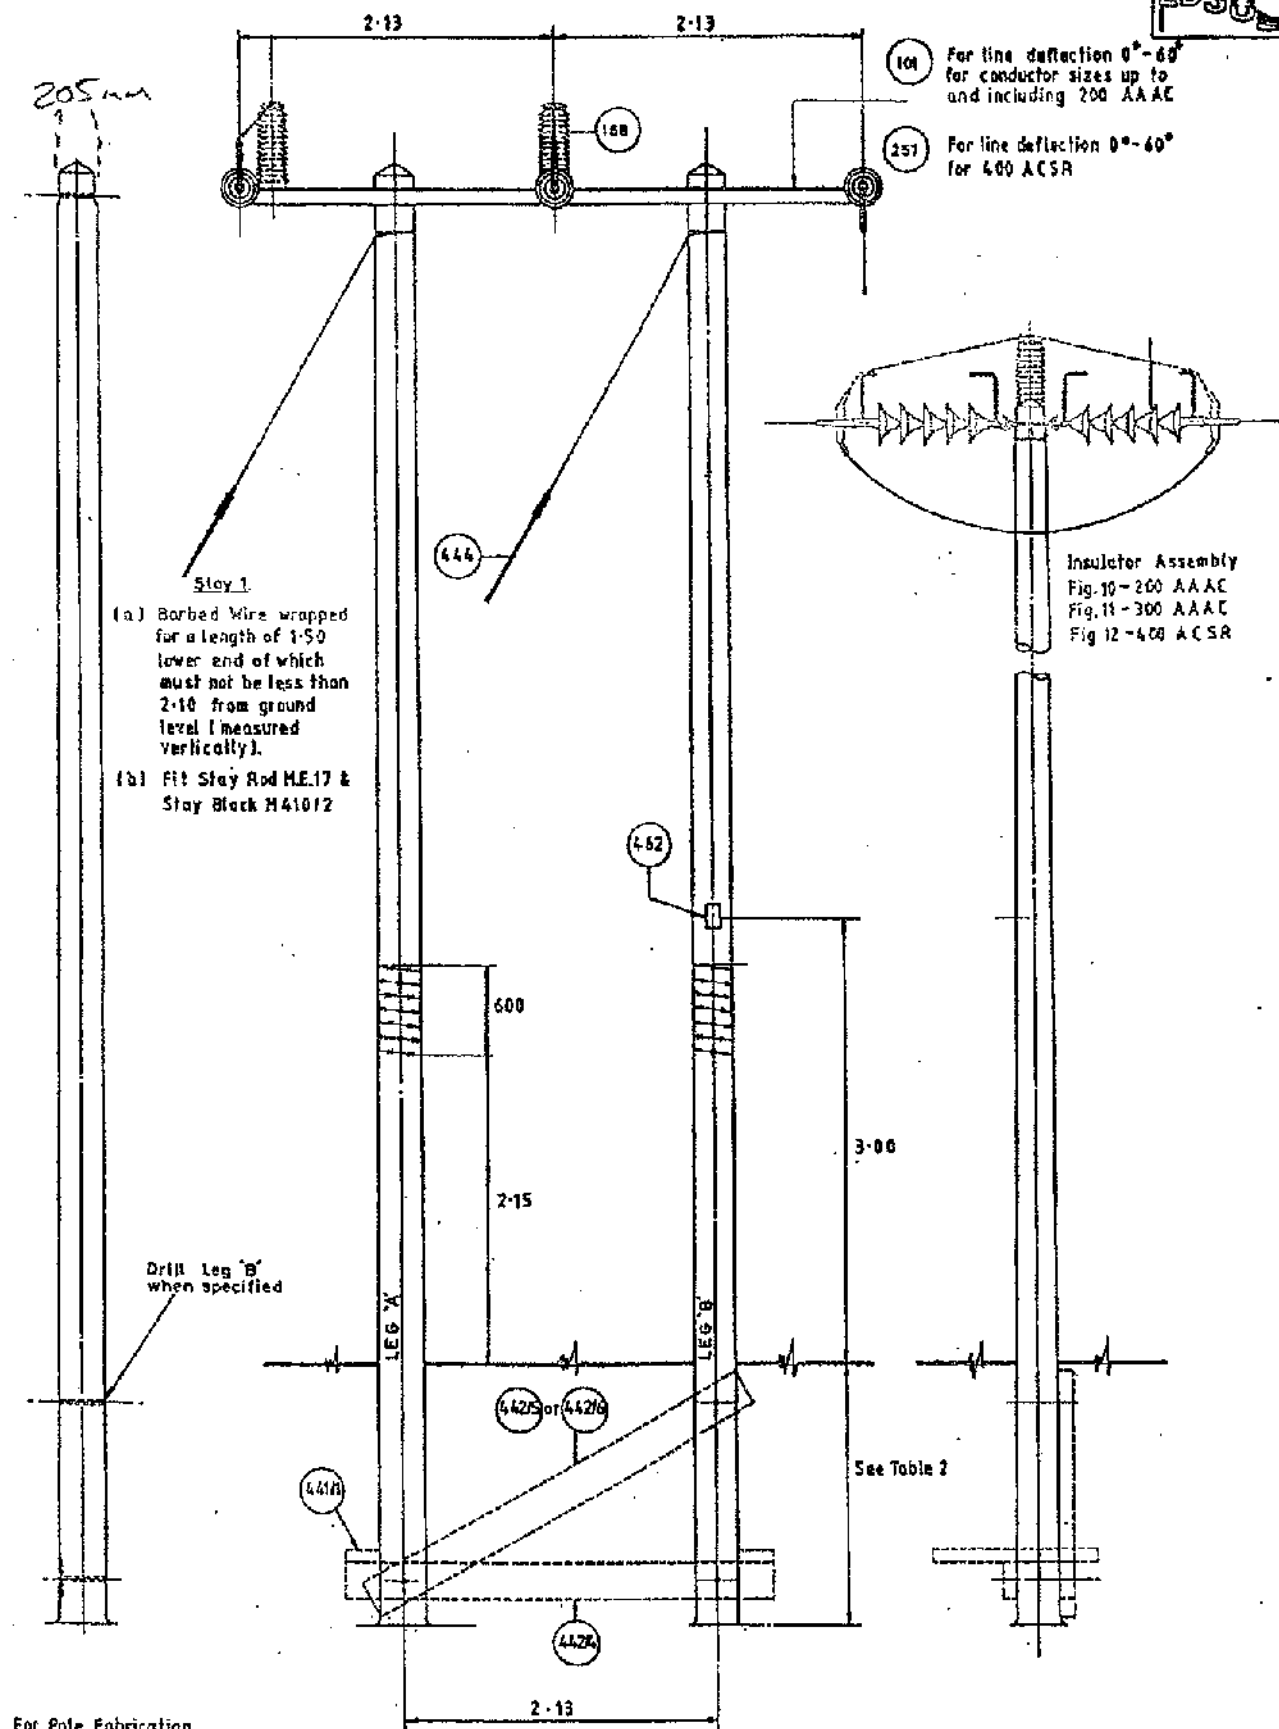

AS DRG MP 1413

66 kV CONSTRUCTION 'H' SECTION POLE

SCALE	
DATE	27-5-92
DRAWN	E.A.H.
TRACED	J.P.
CHECKED	
APPROVED	

MEB
Midlands Electricity plc

FIG. 4.