


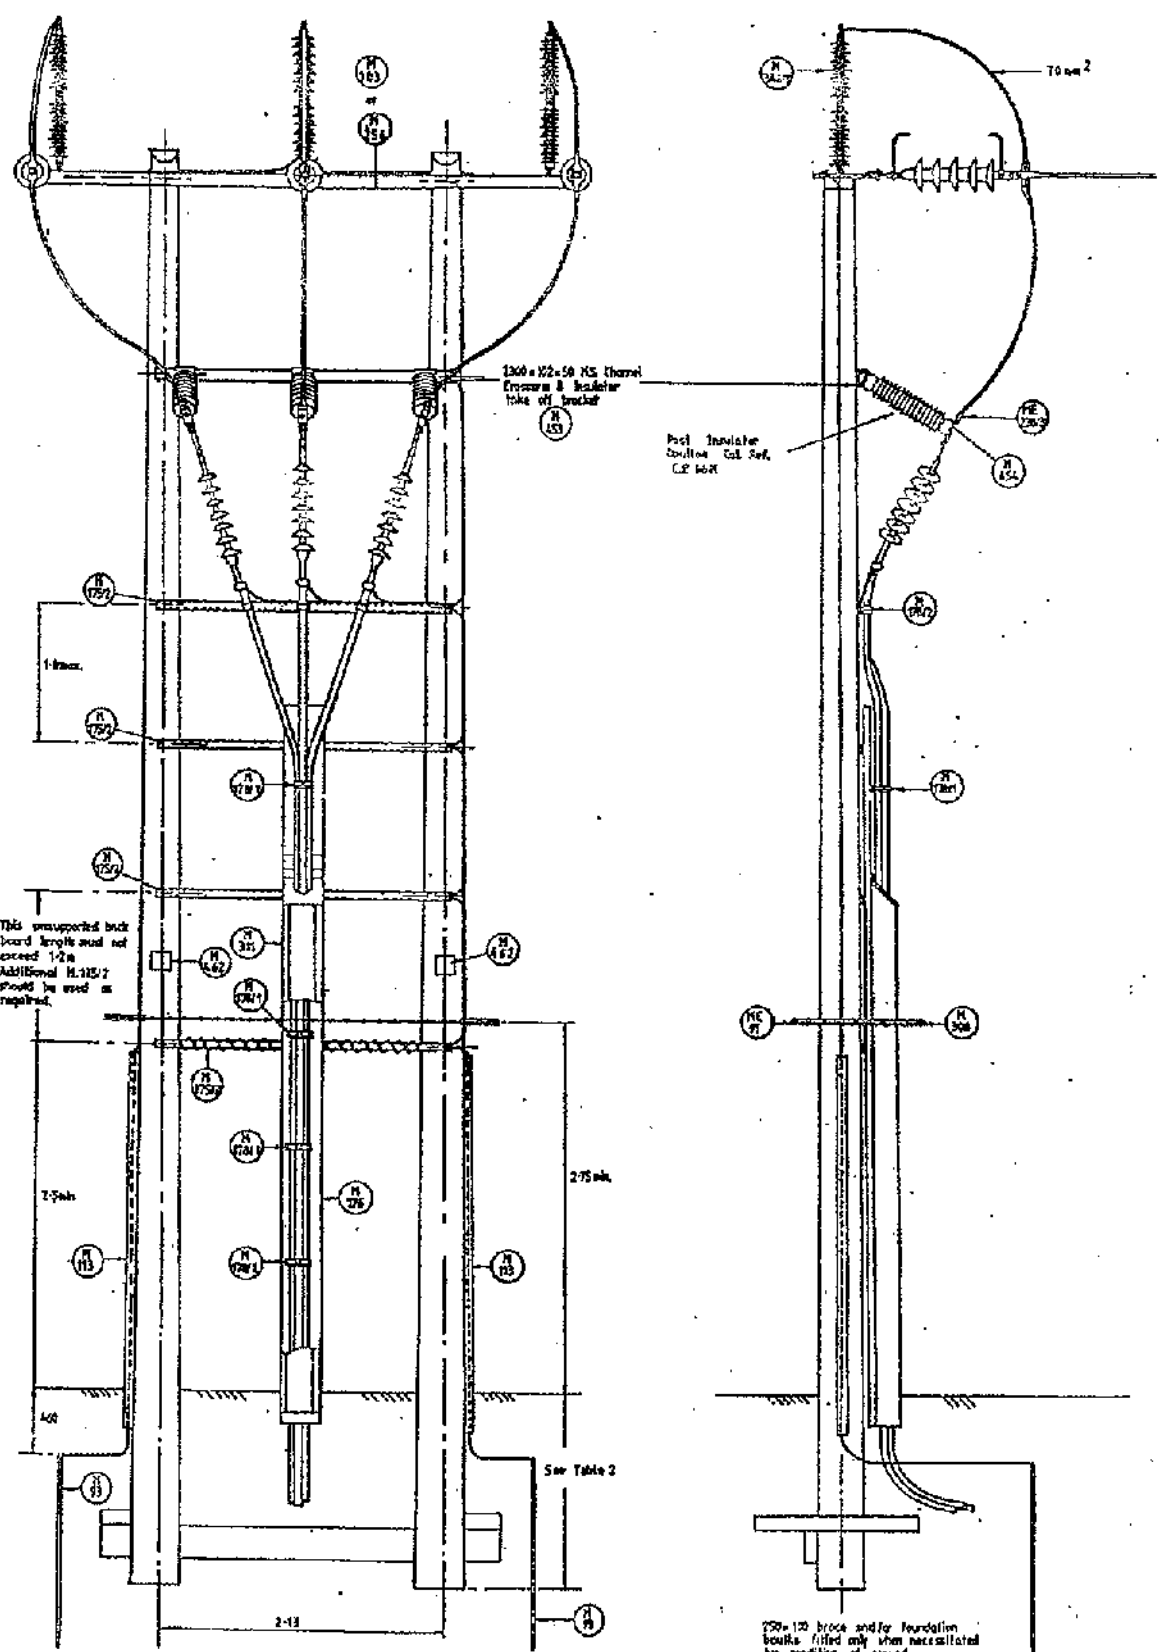

|          |         |   |        |
|----------|---------|---|--------|
| SCALE    |         | <b>66 kV. CONSTRUCTION</b><br><b>CABLE TERMINAL POLES XLP CABLES</b><br><b>MEB</b><br>Midlands Electricity plc | FIG. 6 |
| DATE     | 17.5.92 |   |        |
| DRAWN    |         |   |        |
| ENLARGED |         |   |        |
| CHECKED  |         |   |        |
| APPROVED |         |   |        |