


APPENDIX A3 - General Arrangement Pole Drawings

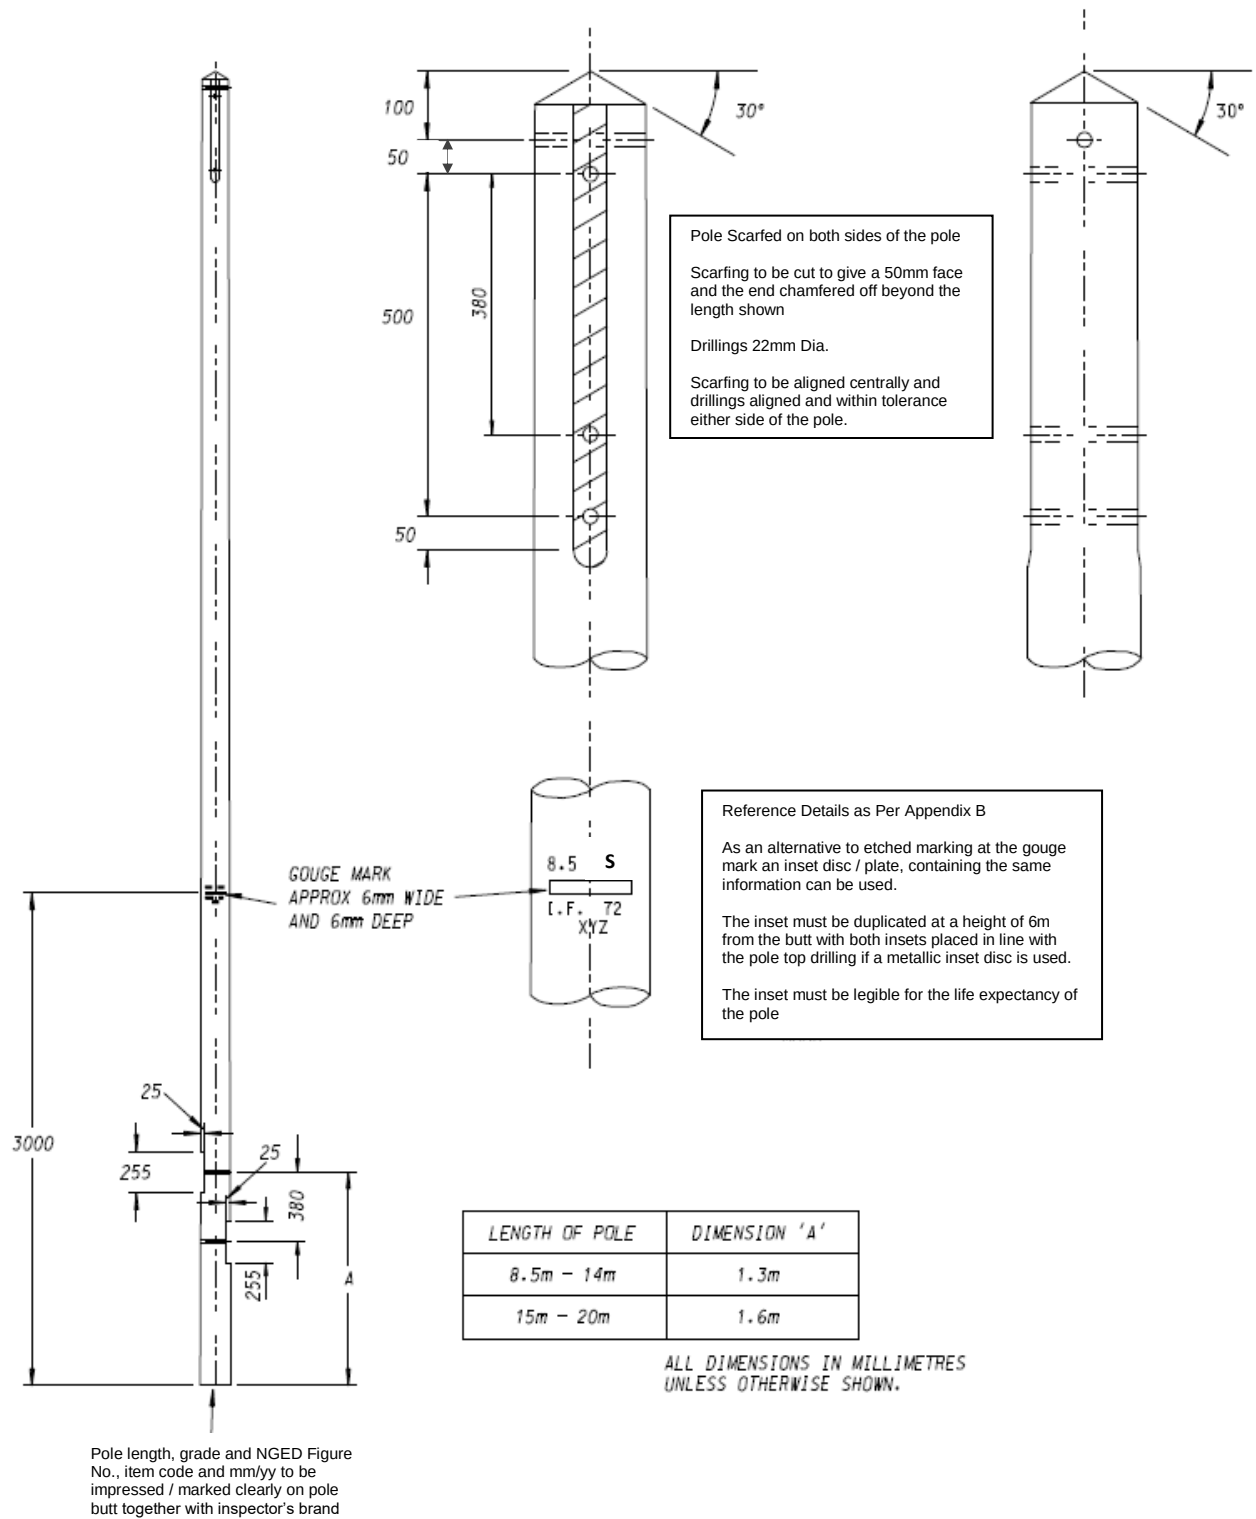

OH4T Fig 1 - Single Pole Drillings, Scarfing & Marking