
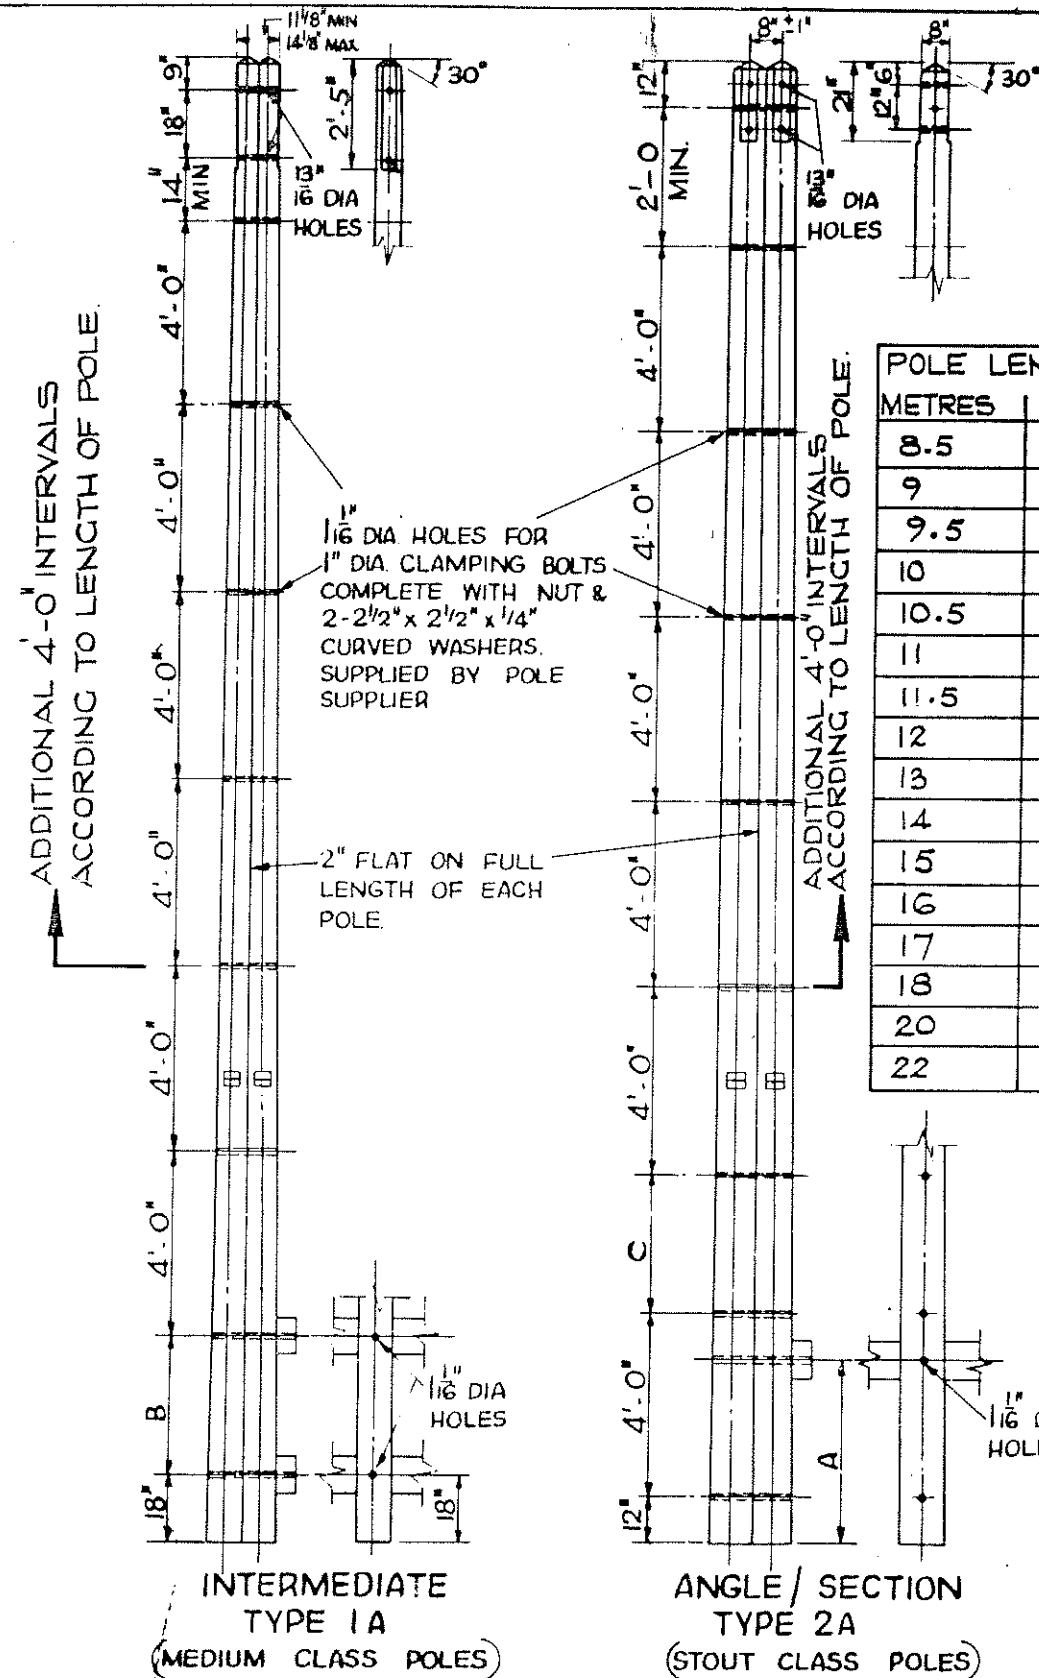


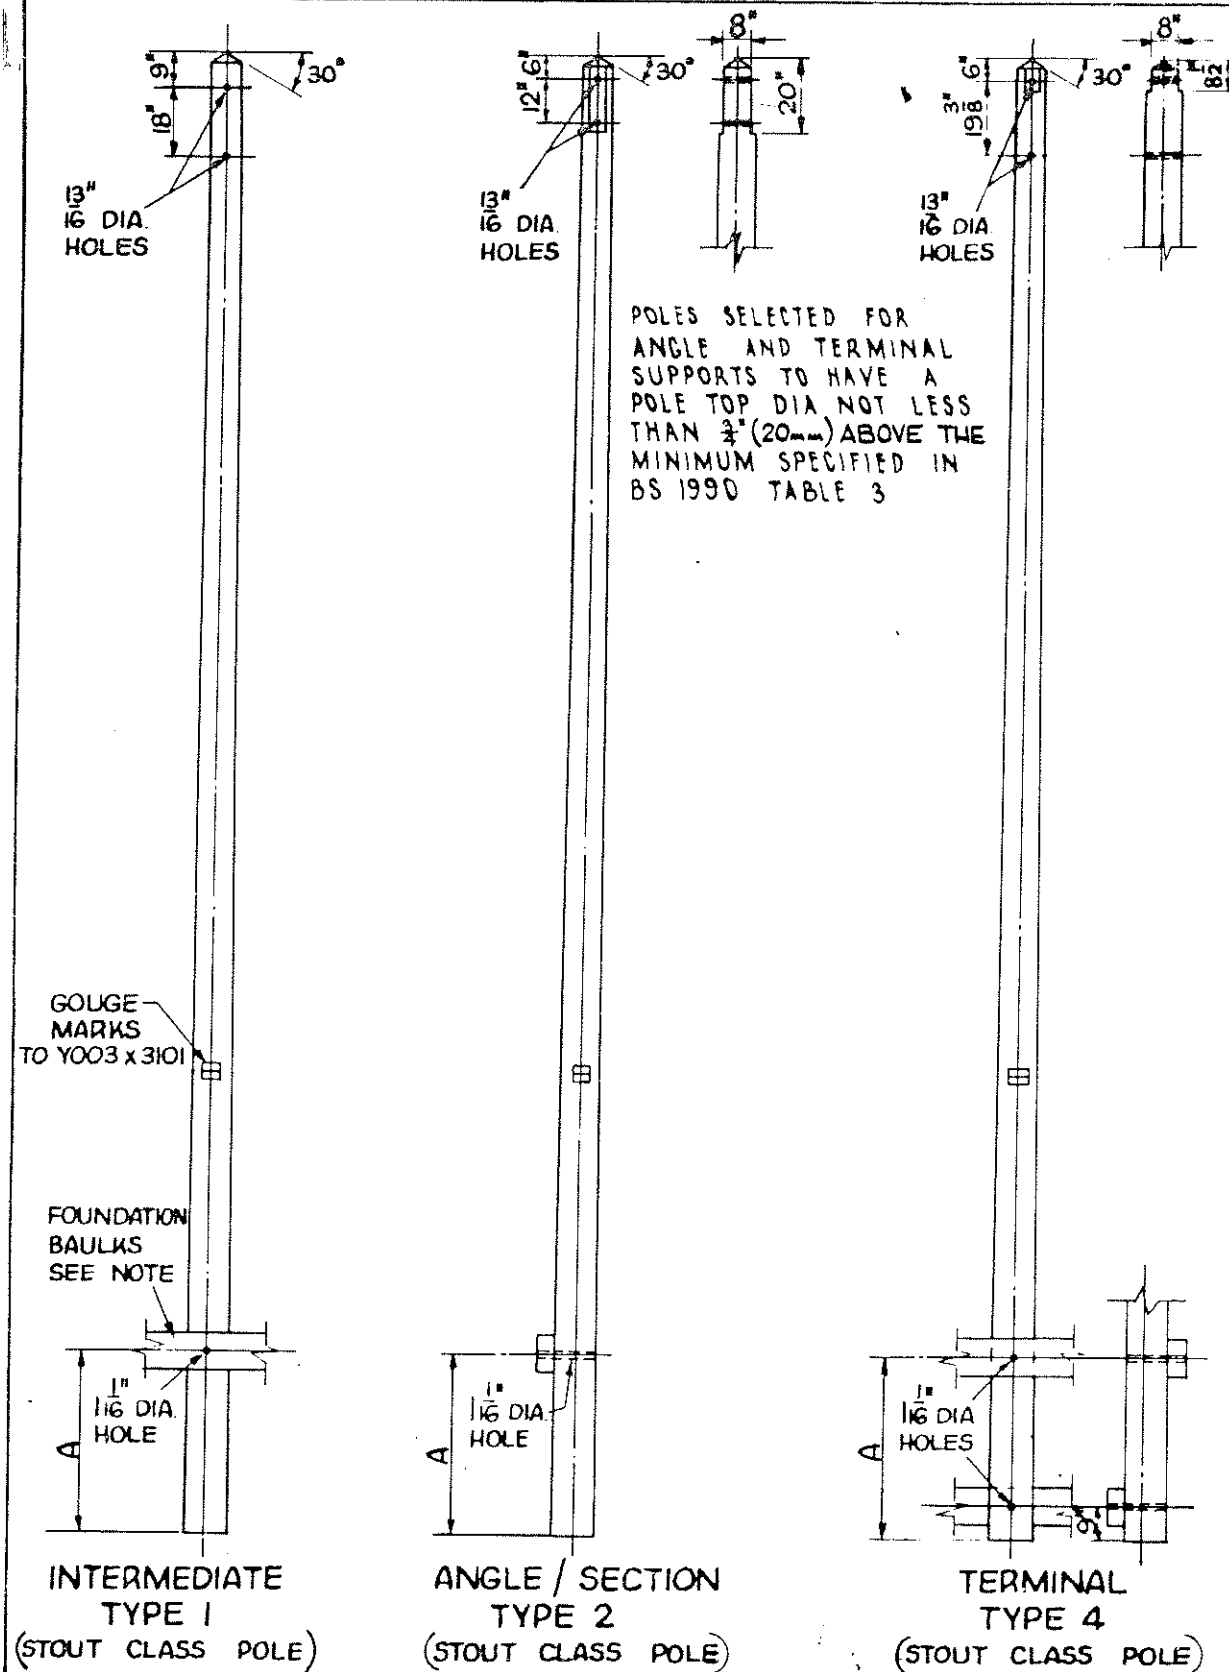

POLE LENGTH METRES	FEET	DIM 'A'	DIM 'B'	DIM 'C'
8.5	28'-0"	4'-0"	3'-0"	3'-0"
9	30'-0"	4'-0"	3'-0"	4'-0"
9.5	32'-0"	4'-0"	3'-0"	3'-0"
10		4'-0"	3'-0"	3'-0"
10.5	34'-0"	4'-0"	3'-0"	4'-0"
11	36'-0"	4'-0"	3'-0"	3'-0"
11.5	38'-0"	4'-0"	3'-0"	4'-0"
12	40'-0"	4'-6"	3'-6"	3'-0"
13	42'-0"	4'-6"	3'-6"	4'-0"
14	45'-0"	5'-0"	4'-0"	4'-0"
15	50'-0"	5'-0"	4'-0"	4'-0"
16		5'-6"	4'-6"	3'-0"
17	55'-0"	5'-6"	4'-6"	3'-0"
18		6'-0"	5'-0"	3'-0"
20		6'-0"	5'-0"	4'-0"
22		6'-0"	5'-0"	3'-0"

POLE APPLICATION				
SUPPORT	11kV CE/C/31	33kV CE/C/36	SCA	SCA
INTER	1	1	1	1A
ANGLE / SECTION	2	2	2A	2A
TERMINAL	4			

MATERIALS

POLES TO BS 1990.

BOLTS TO BS 916 THREADED B.S. WHIT. GALVANISED TO BS 729.

CREOSOTING TO BS 918 RUEPING PROCESS.

TWIN POLES TO BE BOLTED TOGETHER BEFORE CREOSOTING WITH NUTS SLACKENED 2 FULL TURNS. NUTS FULLY TIGHTENED AFTER CREOSOTING.

NOTE FOUNDATION BAULKS TO Y003 x 3201 (TYPE 2)
POLE DRILLED ONLY WHEN BAULKS REQUIRED

drawn E.W.
traced J.M.W.
checked
date 2.4.69
scale 1/4" = 1'

HV OVERHEAD LINES

POLE DETAILS FOR SINGLE SUPPORT LINES
UNEARTHED CONSTRUCTION

A TYPE NO. OF POLES
MODIFIED R.S.5

B TABLE MODIFIED, HEIGHT TO GOUGE MARK REMOVED
NOTES, ADDED NF 3.6.77

Yorkshire Electricity Board

Y003 X 3102