

MATERIALS LIST.


Item	Nº	Commodity Code	Description	Drawing or Ref.Number	M 20 Bolts	Washers		
7	2	BPC 024	Wood Pole	Y204 L 0602		sc	sf	r
19	2	217497	Brace Block	Y204 L 0301	4(Pole)	4	4	
32	1	223669	Crossarm Member	Y204 L 0904	4 x 300'			
60	3		33kV Tension Set	Y204 L 0704				
			66kV Tension Set					
70	2	294181	Safety Sign	Y201 L 1002				
71			Operational Plates	Y201 L 1001/7				
73	4		Stay Arrangement	Y204 L 0501				
74	1	224519	Anti- Climbing Guard	Y201 L 1101/2				
90	1	227173	33kV Sealing End P-form	Y204 L 0907	10(Pole)	10		
94	1	224535	Cable Guard	Y204 L 0911	4 x 50			
95	1		Link Box	Eng Rec C55				
97	1		33kV Cable Supports	Y204 L 0915	8(Pole)			

* 4 off M20 x 60 bolts also required for gusset plates.

Pole Planting Depth	
Pole Length (m)	Dim S (m)
<=11.5	1.80
12.0 - 13.0	2.00
14.0 - 15.0	2.10
16.0 - 17.0	2.25
18.0 - 20.0	2.40

Area:
 File:
 Plotted on: by:

Copyright of YORKSHIRE ELECTRICITY GROUP plc. No part of this drawing to be reproduced without prior permission.

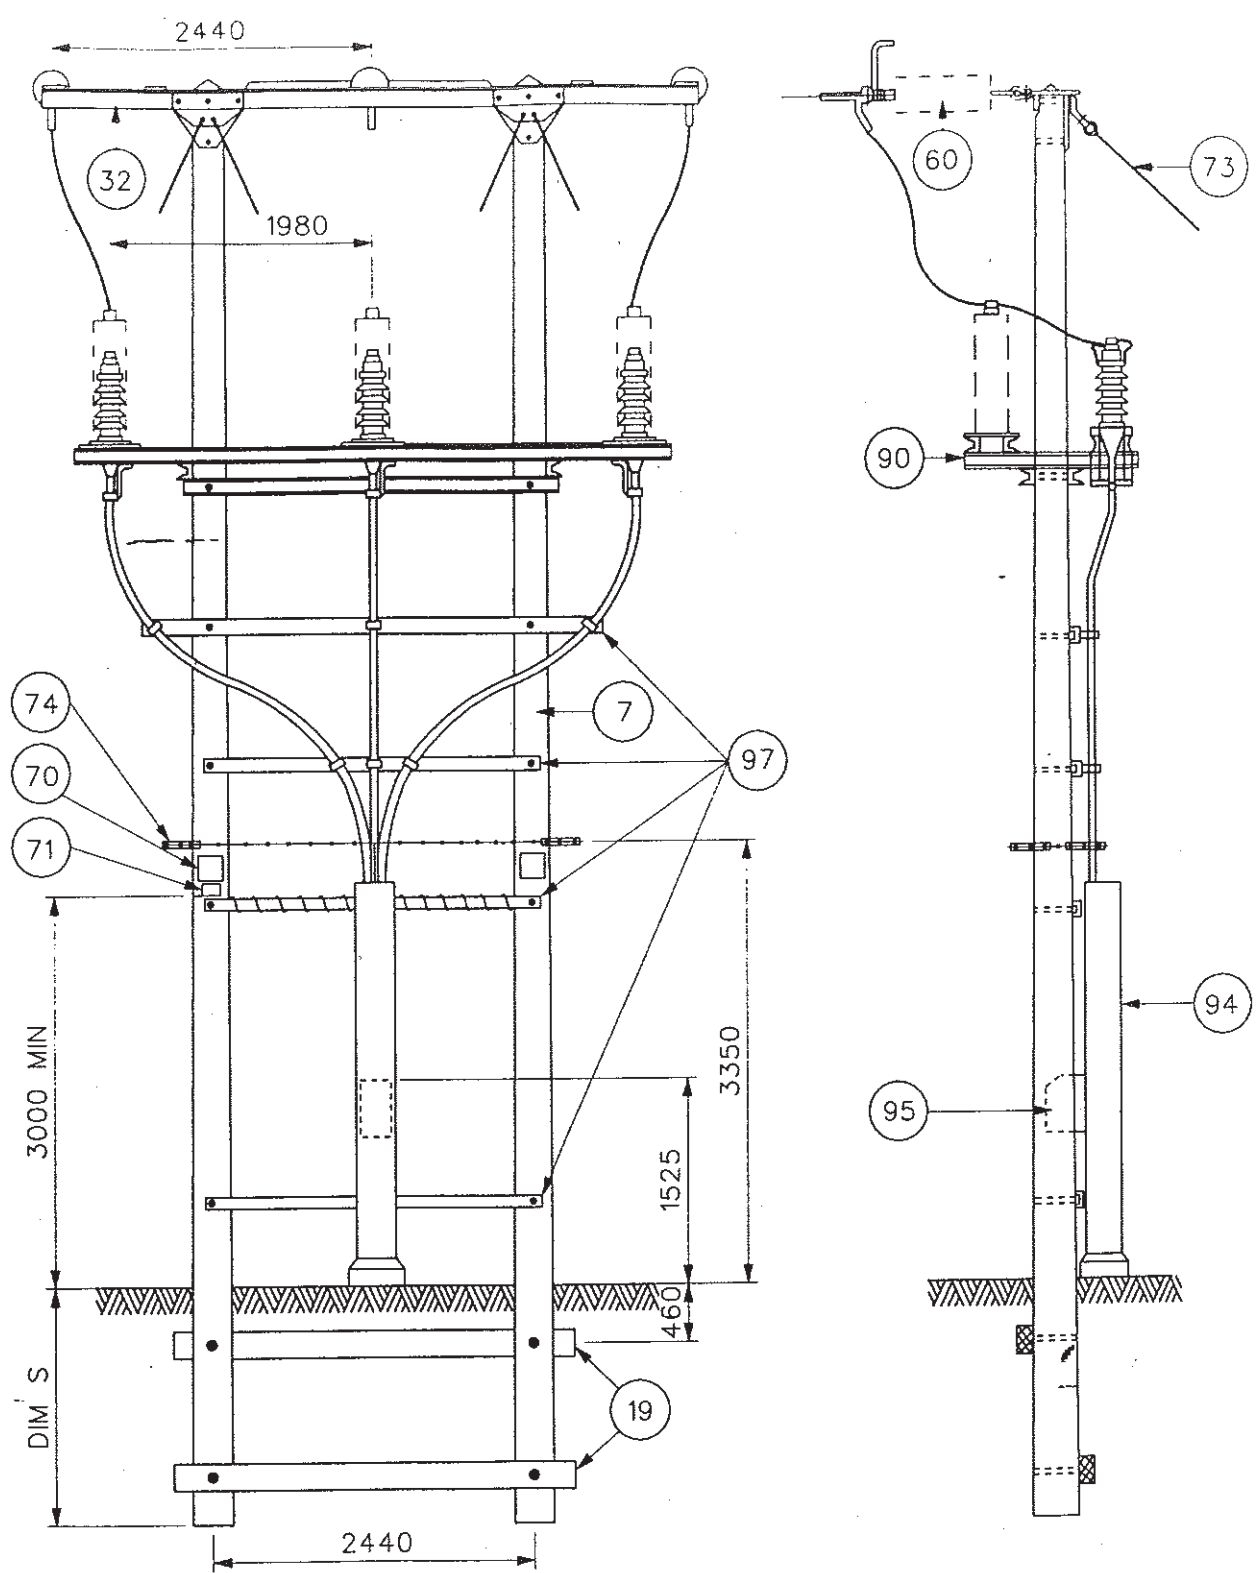

DIMENSIONS IN MILLIMETRES

drawn	BT	GENERAL ARRANGEMENT		
traced	IPM	CE/C/37 (M1) CE/OM/DC1 33kV CABLE TERMINATION WITH SURGE DIVERTERS		
checked	JMP			
approved				
revision	B	date	18.5.98	original scale NTS
		Y104L0117		CAD

