
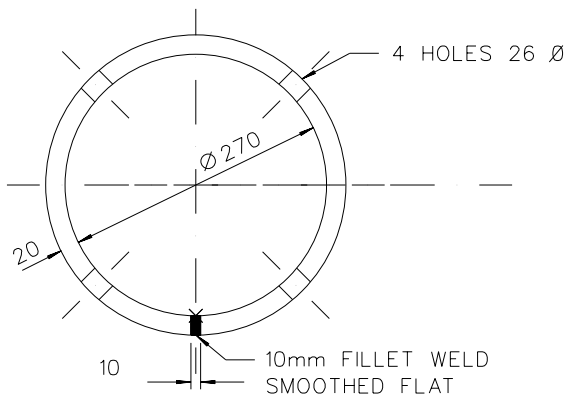


ITEM 1


ELEVATION

SIDE ELEVATION

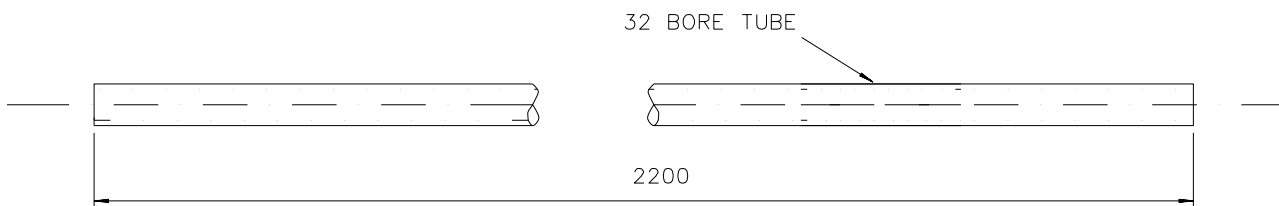

ITEM 2


PLAN

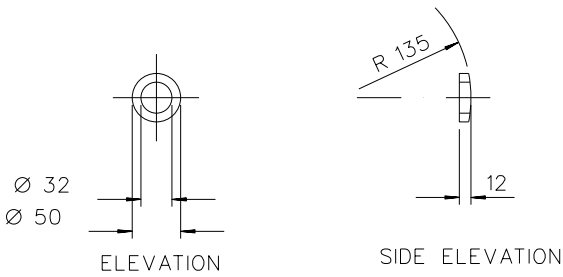

ITEM 3

ELEVATION


SIDE ELEVATION

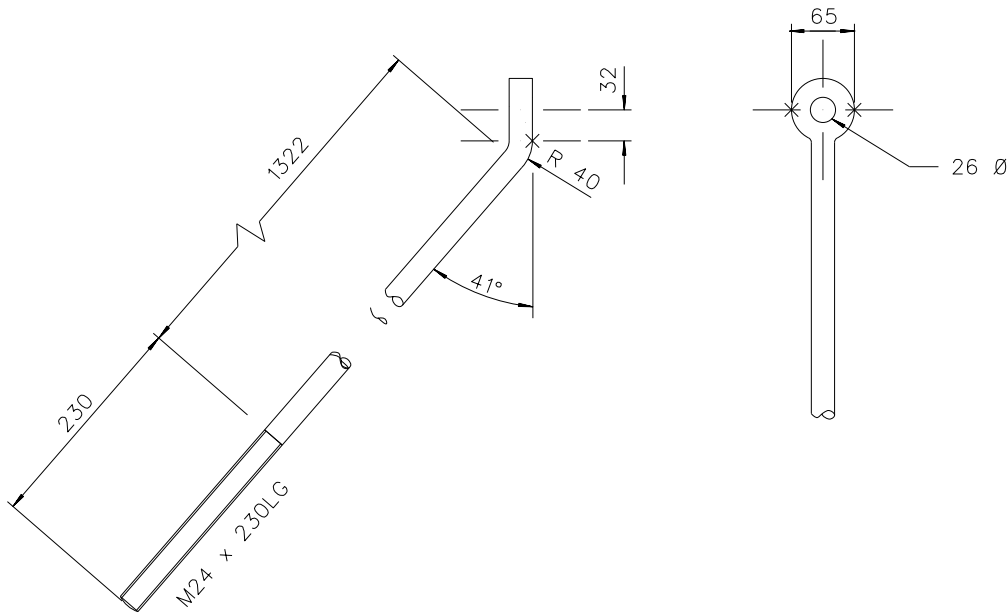

ITEM 4
25 mm MS ROD COMPLETE
WITH TWO NUTS AND TWO
WASHERS

ELEVATION

SIDE ELEVATION

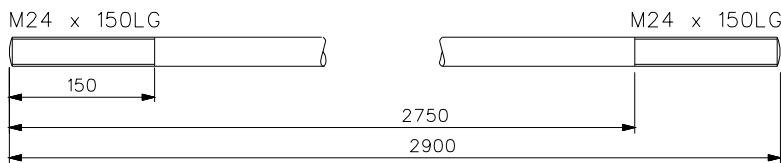

ITEM 5
25mm MS ROD COMPLETE
WITH TWO NUTS AND FOUR
(75x75x6) WASHERS

PLAN

MATERIALS
TUBE - SEAMLESS STEEL ,
HEAVY CLASS , TO BS 1387
OTHER COMPONENTS - MILD
STEEL ,TO BS 4360 GRADE 43A
ALL MATERIALS TO BE
GALVANISED TO BS 729
ALL NUT AND ROD THREADS
TO BS 3643

PARTS LIST

	ITEM	1	2	3	4	5
NUMBER	SINGLE BRACING	1	2	4	4	2
REQUIRED	DOUBLE BRACING	2	3	8	8	3

 CE Electric UK		Lloyds Court, 78 Grey Street, Newcastle Upon Tyne, NE1 6AF			
Manufacturer Details		OVERHEAD LINES POLE BRACINGS CE / C / 37M			
Sheet No. 1	Scale N.T.S.				
Prepared By Janis,Webb		Type OVERHEAD LINES			
Revised 29/05/07	Grid Reference	Ref No.	C948774	Historic Drg.No.	Y204L0905
Date Issued 25/05/07	Checked By	Revision B Notes			